ДЕМОНСТРАЦИОННЫЙ ОБРАЗЕЦ. Расчёт выполнен автоматически по данным анкеты; до передачи заказчику подлежит проверке инженером.

Теплотехнический расчёт наружной стены

Объект: Дом 8×10 м по наброску заказчика. Место строительства: с. Вознесенка. Назначение — индивидуальный жилой дом. Конструкция: газобетонная кладка на клею с наружным утеплением — «газобетон D500 400 мм + каменная вата 50 мм».

1. Нормативная база

- СП 50.13330.2024 «Тепловая защита зданий» — п. 5.1, 5.2, формулы (5.1), (5.2), табл. 2–5, прил. М;
- СП 131.13330.2025 «Строительная климатология» — табл. 5.1;
- ГОСТ 30494-2011 «Здания жилые и общественные. Параметры микроклимата в помещениях» — табл. 1.

2. Исходные данные

Климат	метеостанция Челябинск (Сосновский р-н; ближайшая метеостанция — Челябинск), СП 131.13330.2025, табл. 5.1
Температура наиболее холодной пятидневки, обеспеченность 0,92	$t_н$ = −31 °C
Отопительный период (среднесуточная ≤ 8 °C): средняя температура / продолжительность	$t_{от}$ = −6,2 °C; $z_{от}$ = 209 сут
Расчётная температура внутреннего воздуха — минимум оптимальной для жилой комнаты (ГОСТ 30494-2011, табл. 1; район с пятидневкой −31 °C и ниже)	$t_в$ = 21 °C
Зона влажности (СП 50.13330.2024, прил. А) / влажностный режим помещений	сухая (3) / нормальный
Условия эксплуатации ограждающих конструкций (табл. 2)	А
Коэффициенты теплоотдачи: внутренней поверхности (табл. 4) / наружной	$\alpha_в$ = 8,7; $\alpha_н$ = 23 Вт/(м²·°C)

3. Требуемое сопротивление теплопередаче

$$ГСОП = (t_в - t_{от}) \cdot z_{от} = (21 - (-6{,}2)) \cdot 209 = 5\,685 \text{ °C·сут/год}$$

$$R_0^{тр} = a \cdot ГСОП + b = 0{,}00035 \cdot 5\,685 + 1{,}4 = 3{,}39 \text{ м²·°C/Вт}$$ (табл. 3, поз. 1.1, стены)

$$R_0^{норм} = R_0^{тр} \cdot m_p = 3{,}39 \cdot 1{,}0 = 3{,}39 \text{ м²·°C/Вт}$$ (формула 5.1; m_p = 1 — без снижения)

4. Конструкция стены и её сопротивление теплопередаче

№	СЛОЙ (ИЗНУТРИ НАРУЖУ)	Δ, ММ	$\Lambda_Д$, ВТ/(М·°С)	R = Δ/Λ
1	Ячеистый бетон автоклавного твердения D500 СП 50.13330.2024, табл. М.1 поз. 192	400	0,152	2,63
2	Минераловатные изделия из каменного волокна 125–160 кг/м³ (фасадные плиты) СП 50.13330.2024, табл. М.1 поз. 24	50	0,041	1,22

Внутренняя и наружная отделка в запас не учитываются.

$$R_0^{усл} = 1/\alpha_в + \Sigma\delta/\lambda + 1/\alpha_н = 1/8{,}7 + 0{,}400/0{,}152 + 0{,}050/0{,}041 + 1/23 = 4{,}01\ м^2 \cdot °C/Вт$$

$$R_0 = r \cdot R_0^{усл} = 0{,}90 \cdot 4{,}01 = 3{,}61\ м^2 \cdot °C/Вт$$

r — коэффициент теплотехнической однородности, учитывающий углы, оконные откосы, перемычки и узлы опирания перекрытия. Принят r = 0,90 по оценке для газобетонной кладки на клею с наружным утеплением; при разработке проектной документации уточняется расчётом удельных потерь теплоты по прил. Г СП 50.13330.2024.

5. Проверка требований

ТРЕБОВАНИЕ	РАСЧЁТ	НОРМА	РЕЗУЛЬТАТ
а) Поэлементное: $R_o \geq R_o^{норм}$ (п. 5.2)	3,61	3,39	выполнено
в) Санитарно-гигиеническое: $\Delta t_o = (t_в - t_н) / (R_o \cdot \alpha_в) \leq \Delta t_н$ (табл. 5)	(21 − (−31)) / (3,61 · 8,7) = 1,7 °C	4,0 °C	выполнено

6. Вывод

> **Наружная стена «газобетон D500 400 мм + каменная вата 50 мм» удовлетворяет требованиям тепловой защиты СП 50.13330.2024 (п. 5.1 а, в): R_o = 3,61 ≥ R_oнорм = 3,39 м²·°С/Вт, запас 6 %; Δt_o = 1,7 °С ≤ 4,0 °С.**

7. Другие варианты стены для этого места строительства

Толщины блока из прайса; для каждой — минимальная толщина утеплителя из ряда 0, 50, 100, 150 мм, при которой выполняется требование а). Выбранный вариант выделен.

БЛОК D500	НАРУЖНЫЙ СЛОЙ	R_o	ЗАПАС К НОРМЕ
300 мм	100 мм	4,11	21 %
400 мм	**50 мм**	**3,61**	**6 %**
400 мм	фасадный блок 150 мм	3,40	0,3 %

8. Ограничения расчёта


- Комплексное требование п. 5.1 б) — удельная теплозащитная характеристика здания (прил. Д) — не проверялось: требует расчёта всех ограждений (окна, кровля, пол, двери) и выполняется в составе проекта.

- Защита от переувлажнения (разд. 8) не проверялась. Для наружного утепления каменной ватой с паропроницаемой отделкой влагонакопление, как правило, не лимитирует; подтверждается расчётом в проекте.
- Расчёт выполнен для глади стены с коэффициентом однородности r; узлы (перемычки, армопояс, опирание плит) детально не моделировались.
- Документ — приложение к эскизному проекту и коммерческому предложению; не является проектной документацией.

Расчёт выполнил: ИНСИ БЛОК

Проверил: ИНСИ БЛОК

План на отм. 0.000 М 1:50

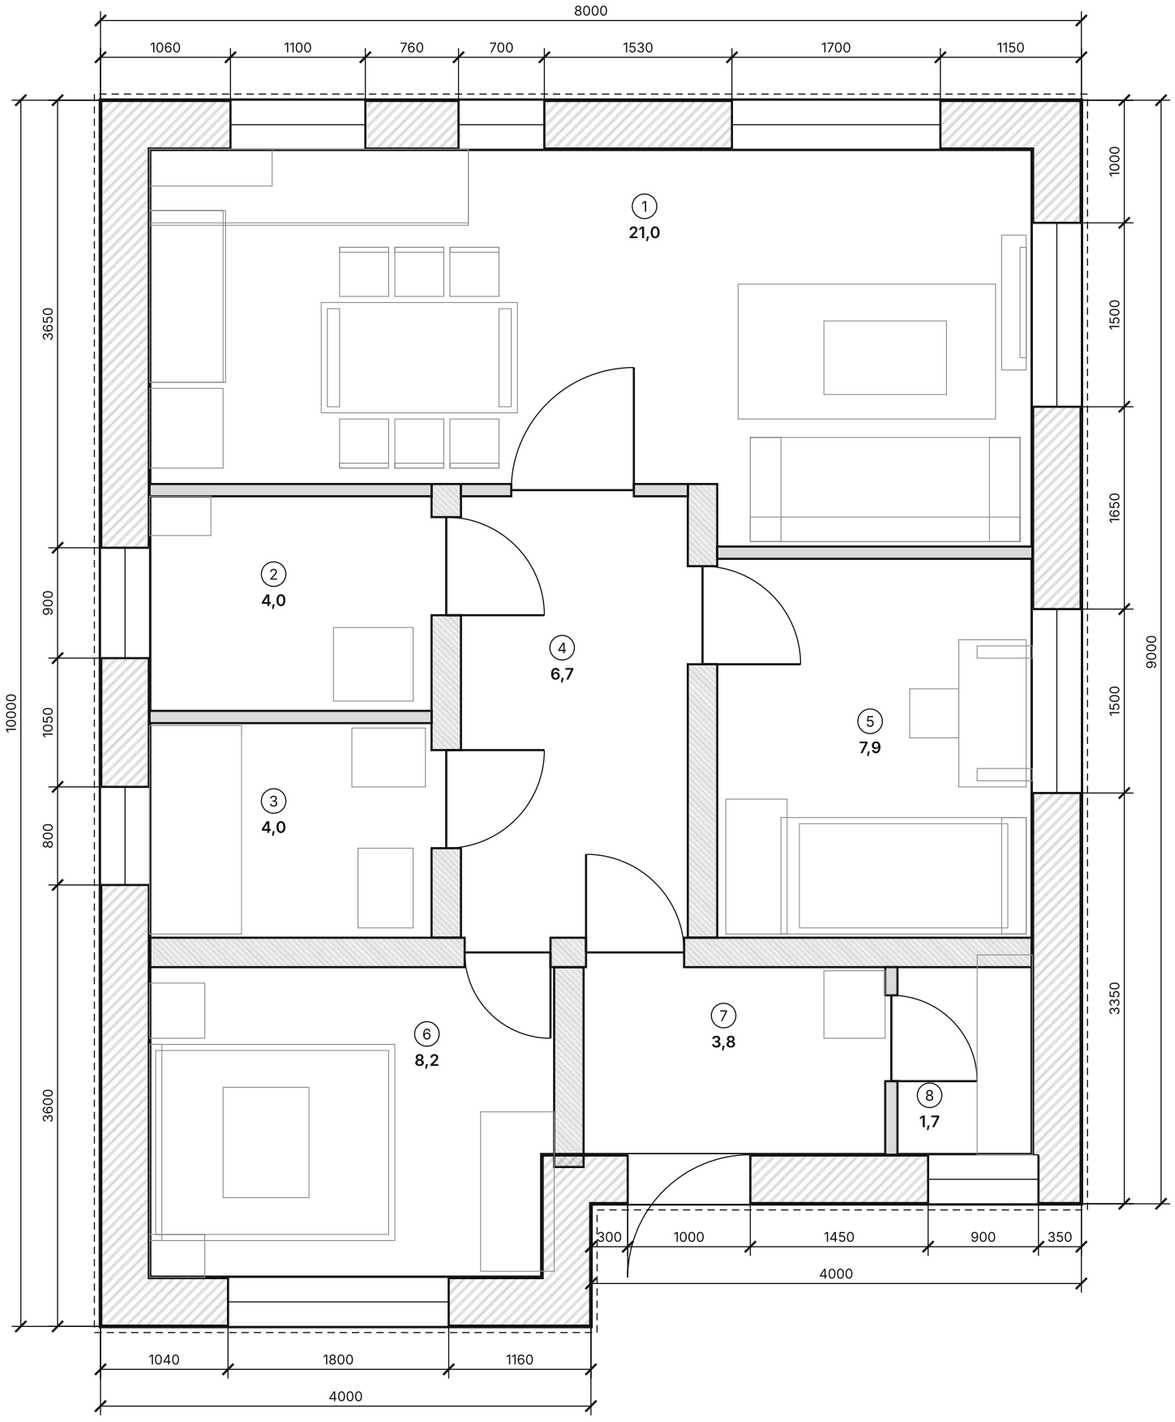

Спецификация газобетона

Поз.	Наименование	Кол.	Ед.	Примечание
1	Блок 625×250×400 D500 B2,5	33,0	м³	наружные стены
2	Блок 625×250×200 D500 B2,5	4,5	м³	фронтоны
3	Блок 625×250×240 D500 B2,5	9,0	м³	внутренние несущие
4	Блок 625×250×100 D500 B2,5	4,5	м³	перегородки, облицовка пояса
5	U-блок 400	33	шт	перемычки наружных стен
6	U-блок 240	15	шт	перемычки дверей в несущих стенах
7	Клей для газобетона, 25 кг	50	меш.	
8	Упаковка (поддон)	34	шт	по прайсу

Экспликация помещений

№	Наименование	Площадь, м²
1	Кухня-гостиная	21,0
2	Котельная / постирочная	4,0
3	Санузел	4,0
4	Холл	6,7
5	Детская	7,9
6	Спальня	8,2
7	Тамбур	3,8
8	Гардероб	1,7
	Итого	57,3

Примечания:

1. Эскиз для расчёта стоимости газобетона. Не является рабочей документацией.
2. Наружные стены - газобетон D500 B2,5 400 мм + минвата 50 мм, R0=3,61 (норма 3,39).
Теплотехника - с. Вознесенка, метеостанция Челябинск (СП 131.13330.2025), СП 50.13330.2024.
3. Объёмы - с запасом 5% на подрезку, целыми поддонами по 1,5 м3.
4. Цены - прайс ИНСИ БЛОК (сверено 22.10.2026): газобетон с упаковкой 357 995 руб.
5. Внутренние несущие - 240 мм, перегородки - 100 мм. Пояс - монолит, облицовка блоком 100.
6. Фундамент, перекрытие, стропила, армирование - по расчёту. Мебель показана условно.

ИНСИ БЛОК · 22.10.2026 · не является рабочей документацией

ДА810-АР

Дом 8×10 м по наброску заказчика


Эскизный проект для расчёта газобетона

План, экспликация, спецификация	Стадия	Лист	Листов
	Э	1	2


Развёртки наружных стен по рядам (вид снаружи), стена 400 мм, М 1:100

целый блок 625 · добор (подрезка) · U-блок · пояс


Схема развёрток

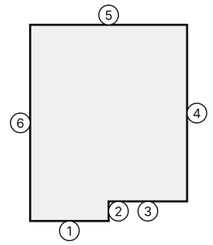


Развёртка 1 — южная стена, 4,00 м · целых 30, доборов 26, U-блоков 1

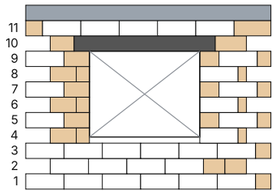


Развёртка 2 — восточная стена, 1,40 м · целых 10, доборов 11, U-блоков 0

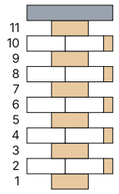


Развёртка 3 — южная стена, 4,40 м · целых 33, доборов 33, U-блоков 2

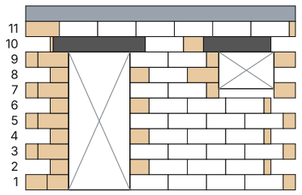


Развёртка 4 — восточная стена, 9,00 м · целых 91, доборов 36, U-блоков 2

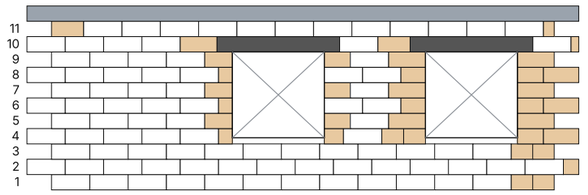

Развёртка 5 — северная стена, 8,00 м · целых 72, доборов 39, U-блоков 3

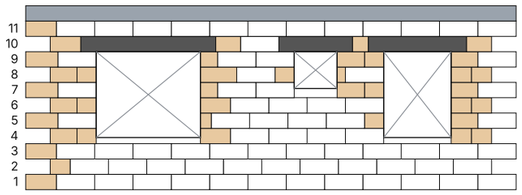

Развёртка 6 — западная стена, 10,00 м · целых 140, доборов 27, U-блоков 2

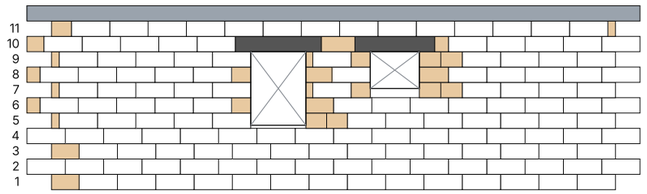

Итого по наружным стенам: целых 376, доборов 172 (31,4 %), U-блоков 10. Ряды по 250 мм, перевязка не менее 100 мм.

Угол перевязывается через ряд: пустое место в начале ряда занимает блок смежной стены.

ИНСИ БЛОК · 22.10.2026 · не является рабочей документацией

ДА810-АР

Дом 8×10 м по наброску заказчика

Эскизный проект для расчёта газобетона

Порядовка наружных стен 400 мм	Стадия	Лист	Листов
	Э	2	2