КОММЕРЧЕСКОЕ ПРЕДЛОЖЕНИЕ · УРОВЕНЬ 2 — ГОТОВЫЙ ПРОЕКТ, ДОРАБОТАННЫЙ ПОД ЗАКАЗЧИКА

Дом Г-210: одноэтажный, 206,5 м², с террасой

Магнитогорск, Челябинская обл. · газобетон ИНСИ D500 B2,5 + кровля



1 044 870 ₽
газобетон + металлочерепица

115,5 м³
блоков, ступень цены от 81 м³

77 поддонов
5 рейса(ов) полуприцепом 12 м

206,5 м²
полезная площадь

> *Заказчик нашёл в интернете проект просторного одноэтажного дома и просит «такой же, но под себя».*

Площадь и характер дома. Состав комнат, стены и кровлю дорабатываем вместе с заказчиком.

Расчёт по прайсу ИНСИ БЛОК с 20.08.2026 для физлиц, самовывоз. Цены и нормы загрузки — данные завода; доставку и итог подтверждает менеджер.

Что дал заказчик и что мы приняли

Принятые решения

- Г-образный дом 16×20,5 м: дневная зона с террасой 28 м², спальное крыло с мастер-блоком
- Наружные стены — газобетон D500, 400 мм + минвата 50 мм (R_o 4,23 при норме 3,32)
- Несущие внутренние — 240 мм, перегородки — 100 мм, армопояс — U-блоки по периметру
- Кровля — две пересекающиеся двускатные, 30°, металлочерепица
- Двери: входная и выход из котельной — наружу; двери санузлов проверены на мебель

Помещения

ПОМЕЩЕНИЕ	М²
Кухня-гостиная-столовая	54,1
Тамбур	4,7
Гардероб	3,3
Холл	25,1
Кабинет / гостевая	14,4
Котельная	3,6
Постирочная	4,2
Кладовая	4,3
Санузел гостевой	5,0
Детская	12,8
Детская	13,6
Коридор	9,5
Гардеробная	8,6
Ванная	6,7
Мастер-спальня	25,9
Гардеробная мастер	5,1
Санузел мастер	5,3
Итого полезная*	**206,5**

* по точным площадям помещений; строки округлены до 0,1 м²

Планировка с расстановкой мебели

План на отм. 0.000 с мебелью



Фрагмент листа Г210-АР, лист 1. Полный комплект чертежей — в приложенных PDF и DWG.

02 · СПЕЦИФИКАЦИЯ И СТОИМОСТЬ

Газобетон, U-блоки, клей, кровля

ПОЗИЦИЯ	КОЛ-ВО	ЦЕНА	СУММА
Блок 625×250×400 D500 B2,5 — наружные стены	70,5 м³	5 050 ₽	356 025 ₽
Блок 625×250×200 D500 B2,5 — фронтоны	10,5 м³	5 050 ₽	53 025 ₽
Блок 625×250×240 D500 B2,5 — внутренние несущие	21 м³	5 050 ₽	106 050 ₽
Блок 625×250×100 D500 B2,5 — перегородки	13,5 м³	5 100 ₽	68 850 ₽
U-блок 400 — перемычки наружных стен	57 шт	690 ₽	39 330 ₽
U-блок 400 — армопояс по периметру	120 шт	690 ₽	82 800 ₽
U-блок 240 — пояс и перемычки несущих стен	88 шт	490 ₽	43 120 ₽
Клей для газобетона, 25 кг	116 меш.	365 ₽	42 340 ₽
Итого газобетон и комплектующие			**791 540 ₽**
Металлочерепица «Монтеррей», площадь кровли 329 м²	329 м²	от 770 ₽	253 330 ₽
Итого газобетон + кровельное покрытие			**1 044 870 ₽**

Возвратный залог за поддоны 77 × 250 ₽ = 19 250 ₽ — не входит в итог. Профнастил С-18 вместо металлочерепицы: 266 490 ₽.

Сравнение вариантов

ВАРИАНТ	ГАЗОБЕТОН	ПОДДОНЫ
Принятый, стена 400 мм	791 540 ₽	77
Стена 300 мм	669 655 ₽	65
Принятый, для юрлица	820 415 ₽	77

Разница 121 885 ₽ — решение за заказчиком: толщина стены влияет на теплозащиту и ступень цены.

Теплозащита стены

$R_o = 4{,}23$

при норме 3,32 м²·°C/Вт для Челябинска (СП 50.13330, СП 131.13330). Стена с утеплением 50 мм проходит норму — заказчику не нужно гадать, «хватит ли 300».

Как получена цена

Объём кладки за вычетом окон, дверей и перемычек, +5 % на подрезку, округление до целых поддонов по 1,5 м³. Ступень цены — по объёму стеновых блоков.

Проверено раскладкой блоков по рядам (листы 3–4): наружные стены — 63,8–71,4 м³ против 70,5 м³ в спецификации. Запас 5 % подтверждён.

03 · ЛОГИСТИКА И ВИЗУАЛИЗАЦИЯ

Как привезём и как это будет выглядеть

Отгрузка

Поддонов блоков	77
Рейсов полуприцепом 12 м (18 поддонов)	5
Объём блоков к отгрузке	115,5 м³
Завод → Магнитогорск	≈ 265 км, около 4 часов

U-блоки и клей комплектуются со склада в те же рейсы. Тариф доставки подтверждает логист.

Что дальше

- ✓ Замер участка и подтверждение планировки
- ✓ Фиксация цены и ступени объёма
- ✓ График рейсов под темп кладки
- ✓ Кровля и фасад — отдельным расчётом при необходимости



Вид без кровли: мебель и проходы



Вид со двора



Вход




Общий вид без кровли

Что заказчик получает на руки

- ✓ Это КП с расчётом и логистикой
- ✓ Чертежи: Г210-АР_лист1.pdf (план с мебелью, экспликация, спецификация)
- ✓ Чертежи: Г210-АР_лист2.pdf (фасады, разрез, план кровли)
- ✓ Чертежи: Г210-АР_лист3.pdf (кладочные планы 1 и 2 рядов, ведомость блоков)
- ✓ Чертежи: Г210-АР_лист4.pdf (развёртки стен по осям А и 1)
- ✓ Смета и спецификация в Excel (Г210_Смета_и_спецификация.xlsx)
- ✓ 3D-модель SketchUp с мебелью и рендеры

План на отм. 0.000 (с расстановкой мебели) М 1:100

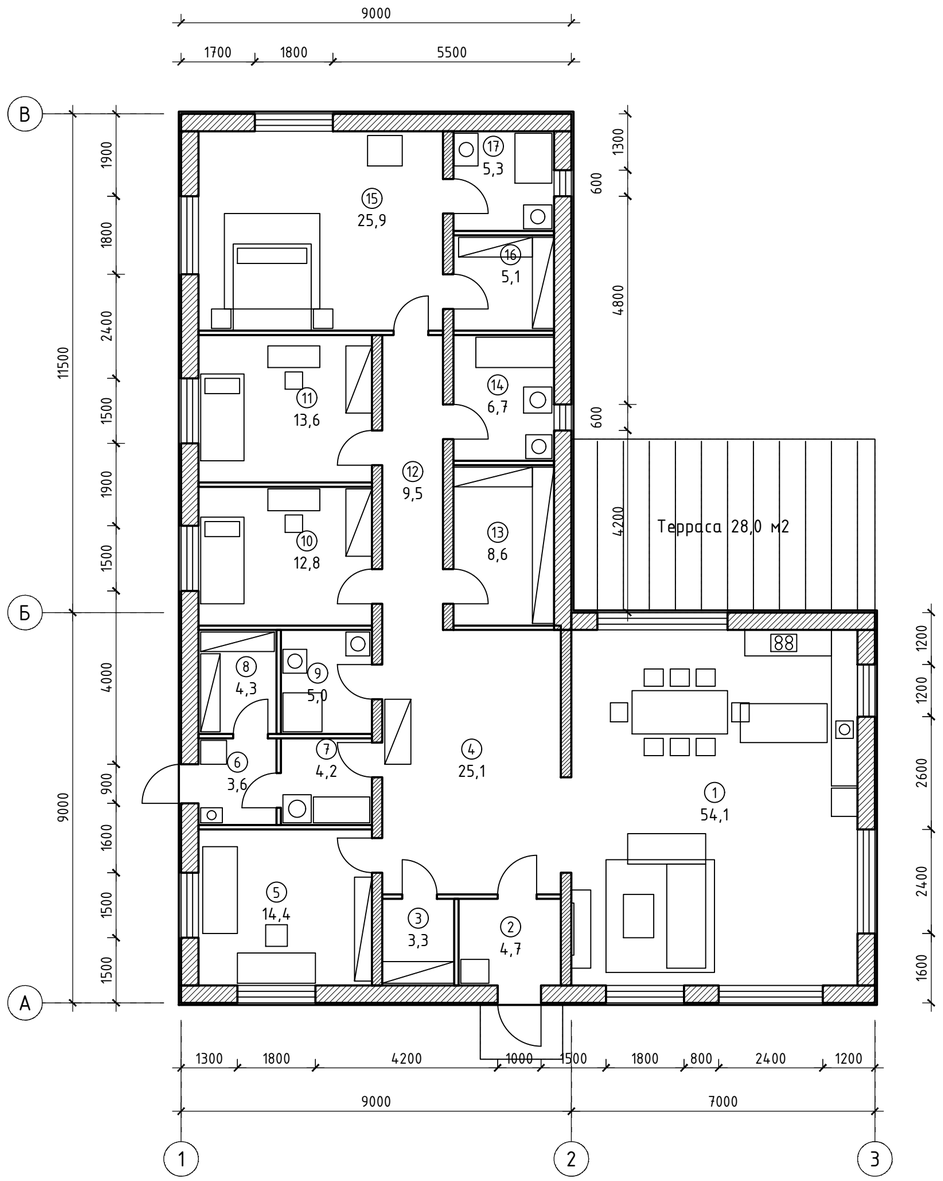

Экспликация помещений

Номер	Наименование	Площадь, м2
1	Кухня-гостиная-столовая	54,1
2	Тамбур	4,7
3	Гардероб	3,3
4	Холл	25,1
5	Кабинет / гостевая	14,4
6	Котельная	3,6
7	Постирочная	4,2
8	Кладовая	4,3
9	Санузел гостевой	5,0
10	Детская	12,8
11	Детская	13,6
12	Коридор	9,5
13	Гардеробная	8,6
14	Ванная	6,7
15	Мастер-спальня	25,9
16	Гардеробная мастер	5,1
17	Санузел мастер	5,3
	Итого полезная	206,5
	Терраса (не входит)	28,0

Спецификация газобетона

Поз.	Обозначение	Наименование	Кол.	Ед.	Примечание
1	ГОСТ 31360-2024	Блок I/625x250x400/D500/B2,5	70,5	м3	наружные стены, 47 подд.
2	ГОСТ 31360-2024	Блок I/625x250x200/D500/B2,5	10,5	м3	фронтоны, 7 подд.
3	ГОСТ 31360-2024	Блок I/625x250x240/D500/B2,5	21,0	м3	несущие внутр., 14 подд.
4	ГОСТ 31360-2024	Блок I/625x250x100/D500/B2,5	13,5	м3	перегородки, 9 подд.
5	ИНСИ БЛОК	U-блок 400	57	шт	перемычки
6	ИНСИ БЛОК	U-блок 400	120	шт	пояс по периметру
7	ИНСИ БЛОК	U-блок 240	88	шт	пояс, перемычки внутр.
8	ИНСИ БЛОК	Клей для газобетона, 25 кг	116	меш.	

Примечания:

1. Эскизный проект для расчёта стоимости газобетона. Не является рабочей документацией.
2. ДЕМОНСТРАЦИОННЫЙ ОБРАЗЕЦ. Не является предложением ИНСИ БЛОК.
3. Наружные стены – газобетон D500 B2,5 400 мм + минвата 50 мм, R0=4,23 (норма 3,32).
4. Несущие внутренние – 240 мм; перегородки – 100 мм; пояс и перемычки – U-блоки.
5. Двери: входная и выход из котельной открываются наружу; двери санузлов – по расчёту вентиляции. Открывание всех дверей проверено на пересечение с мебелью.
6. Объёмы – с запасом 5%, округлены до поддонов 1,5 м3. Прайс ИНСИ БЛОК с 20.08.2026.
7. Фундамент, перекрытие, стропила, армирование – по расчёту. Мебель – условно.

Взам. инв. №


Подп. и дата

Инв. № подл.


Изм.	Кол.уч	Лист	№ док.	Подп.	Дата	Г210-АР			
						Индивидуальный жилой дом Г-210 (демонстрационный эскиз)			
Разраб.						Жилой дом из газобетона, 206,5 м2	Стадия	Лист	Листов
Пров.							П	1	4
Н. контр.						План, экспликация, спецификация			
ГИП									

Формат А2


Фасад 1–3 (главный, южный) М 1:100

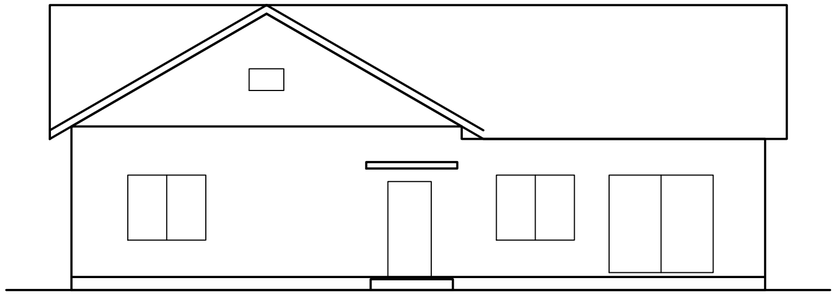


Фасад А–В (восточный) М 1:100

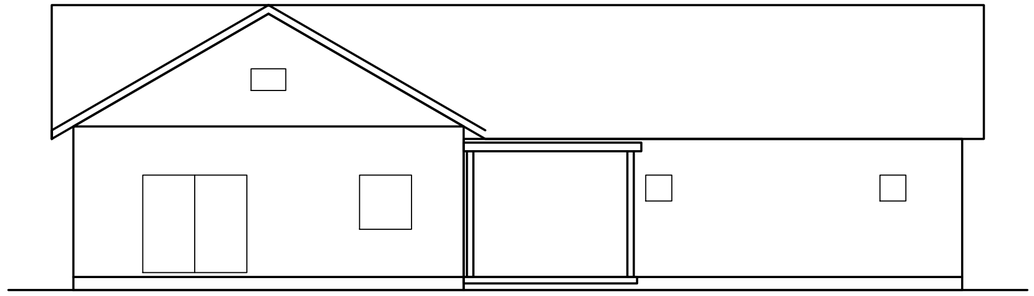

Разрез 1–1 М 1:100

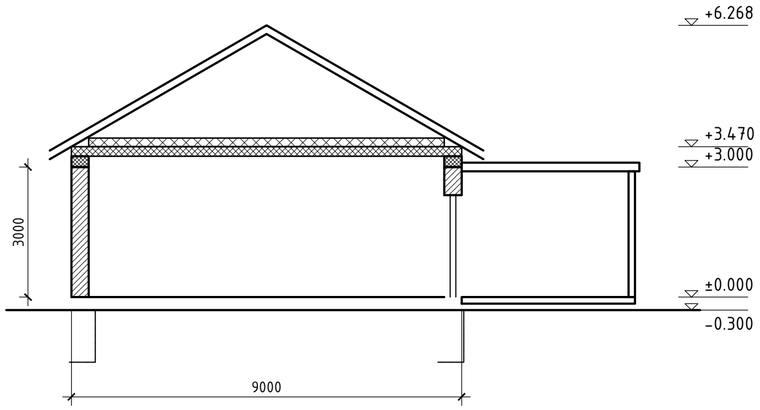

План кровли М 1:200

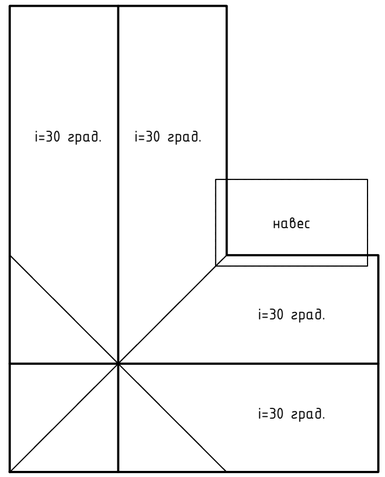


Кровля: металлочерепица ИНСИ по обрешётке и стропилам, 30 град.; ендовы – 4 шт. над центральным блоком (крестовая кровля); водосток по периметру. Площадь кровли ~329 м2.
Навес террасы: металлический каркас, профнастил ИНСИ.

Изм.	Кол.уч	Лист	№ док.	Подп.	Дата	Г210-АР			
						Индивидуальный жилой дом Г-210 (демонстрационный эскиз)			
Разраб.						Жилой дом из газобетона, 206,5 м2	Стадия	Лист	Листов
Пров.							П	2	4
Н. контр.						Фасады, разрез 1-1, план кровли			
ГИП									


Взам. инв. №
Подп. и дата
Инв. № подл.

Формат А2

Кладочный план 1-го ряда (отм. 0.000...+0.250) М 1:100

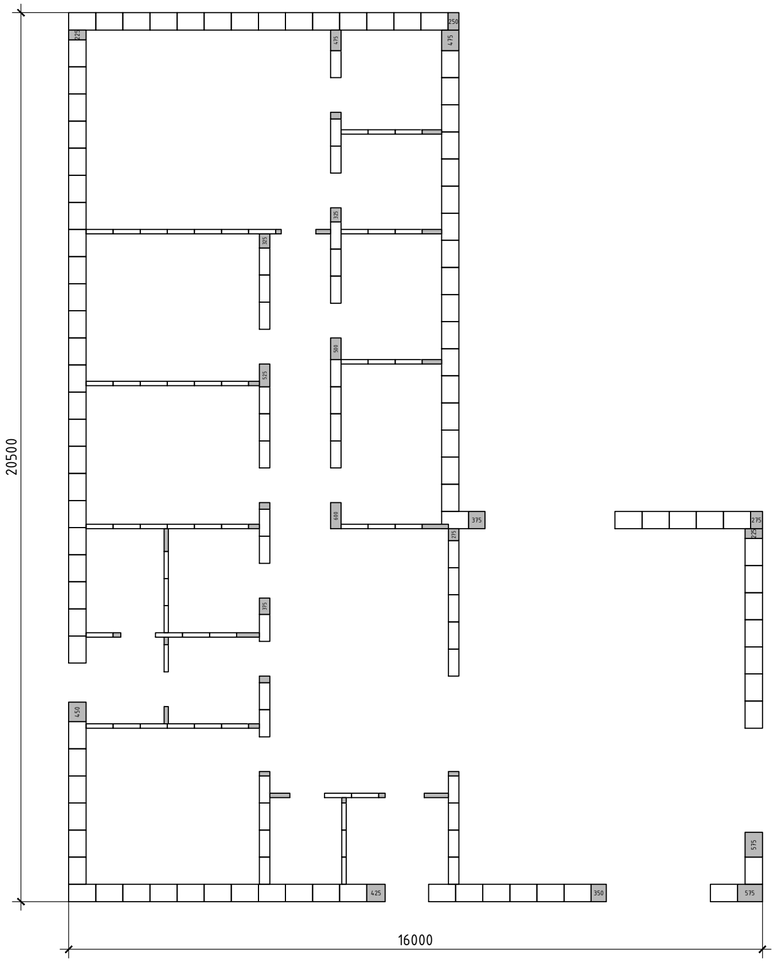

Кладочный план 2-го ряда (отм. +0.250...+0.500) М 1:100

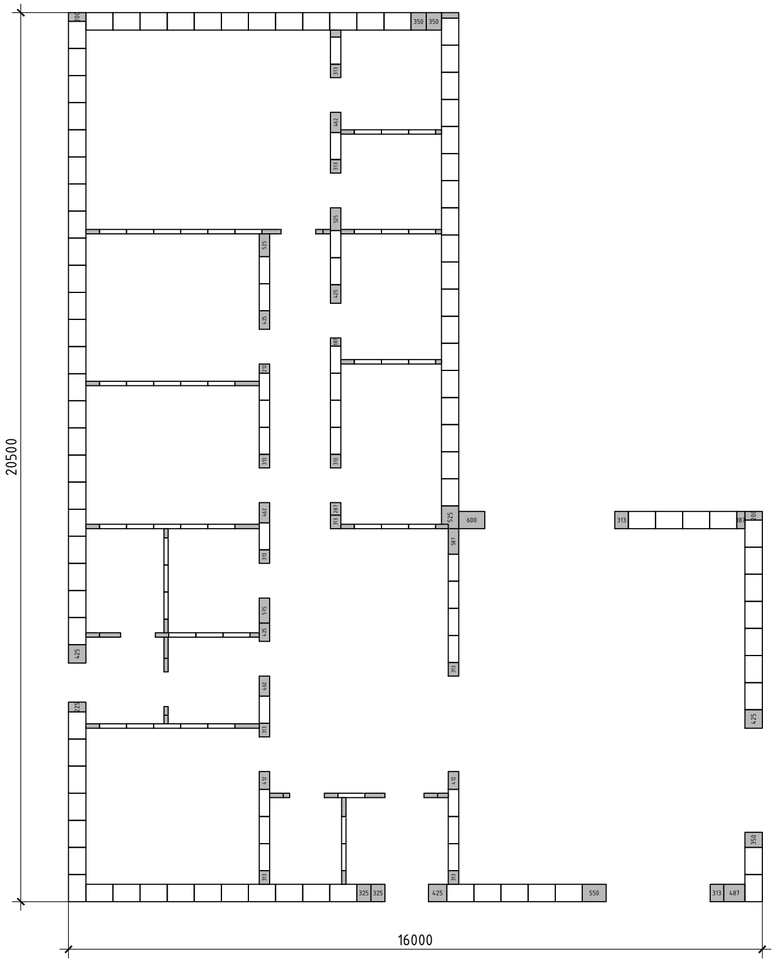

Ведомость блоков по раскладке (12 рядов, до пояса)

Стены	Целых	Доборов	Доля	Блоков, шт	Раскладка, м3	Спецификация
Наружные 400	871	272	23,8 %	1021–1143	63,8–71,4	70,5 м3
Несущие 240	392	198	33,6 %	501–590	18,8–22,1	21,0 м3
Перегородки 100	569	306	35,0 %	730–875	11,4–13,7	13,5 м3

Как читать: нижняя граница – доборы режутся из обрезков, верхняя – каждый добор из нового блока.
Наружные стены: спецификация 70,5 м3 перекрывает экономный вариант (63,8 м3) и на 1,3 % ниже худшего (71,4 м3).
Вывод: запас 5 % в КП подтверждён раскладкой; при раскрое обрезков экономия до 6,7 м3 блока 400 мм.
Доля доборных блоков 24–35 % – аргумент сдвинуть проёмы под модуль блока 625 мм ещё на стадии эскиза.

блок целый 625x250

U-блок перемычки (развёртки)

380 доборный блок (длина, мм)

1. Блоки ИНСИ D500 B2,5: наружные стены 400 мм, внутренние несущие 240 мм, перегородки 100 мм; высота блока 250 мм.
2. Наружные стены перевязываются в углах через ряд: в нечётных рядах проходят стены вдоль осей А–В, в чётных – вдоль осей 1–3. Смещение вертикальных швов – не менее 100 мм.
3. Внутренние стены и перегородки примыкают к наружным; связь – гибкими связями через 2 ряда.
4. Первый ряд – на цементно-песчаный раствор по гидроизоляции; далее – на клей, шов 2–3 мм.
5. Раскладка выполнена автоматически по модели дома; при кладке допускается замена доборов обрезками той же толщины.

Взам. инв. №

Подп. и дата

Инв. № подл.

Изм.	Кол.уч	Лист	№ док.	Подп.	Дата
Разраб.					
Пров.					
Н. контр.					
ГИП					

Г210-АР

Индивидуальный жилой дом Г-210 (демонстрационный эскиз)

Жилой дом из газобетона, 206,5 м2


Стадия	Лист	Листов
П	3	4

Кладочные планы 1-го и 2-го рядов


Организация

Формат А2

Развёртка стены по оси 1 (вид снаружи) М 1:50

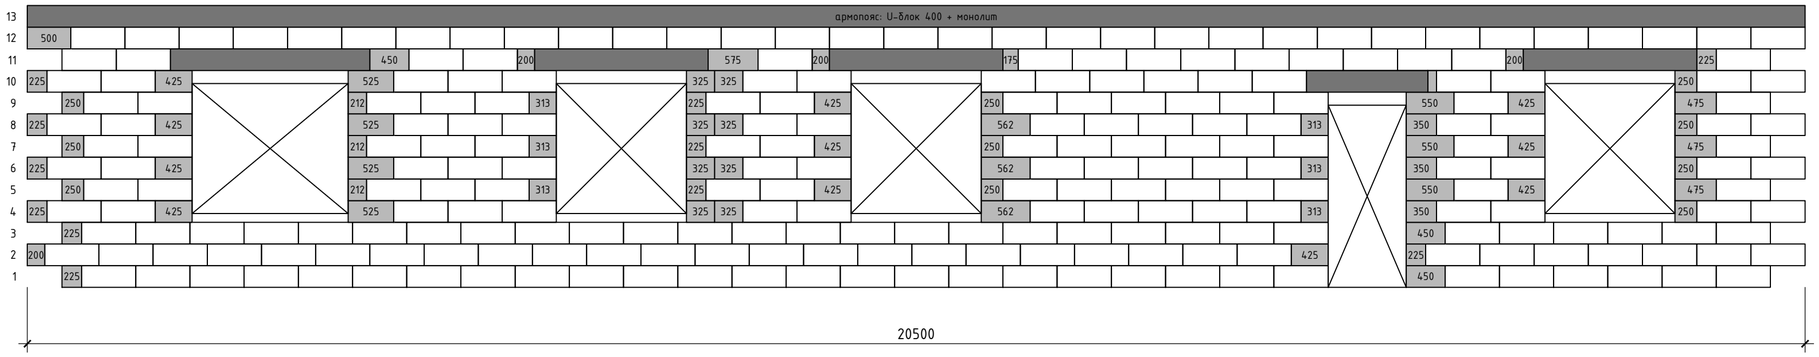

Развёртка стены по оси А (главный фасад, вид снаружи) М 1:50

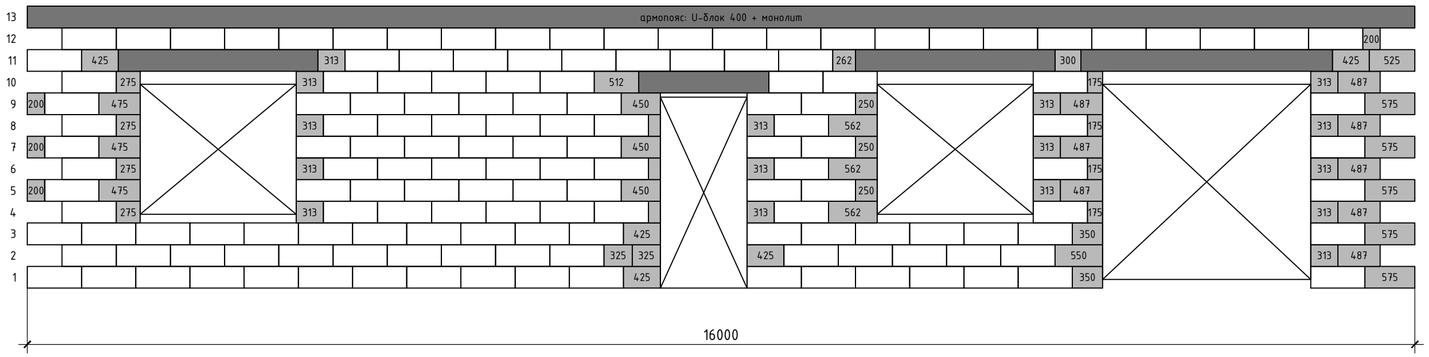

1. Номера рядов – слева; ряд 13 – армопояс из U-блоков с монолитом В15 и арматурой 4d10 А400.
2. Перемычки над проёмами – U-блоки с монолитом, опирание по 250 мм на сторону.
3. Доборы показаны заливкой с длиной в мм. Развёртки остальных стен – по тому же правилу.

Ведомость по раскладке (все стены дома):
наружные 400 – 871 целых + 272 доборов;
несущие 240 – 392 + 198; перегородки 100 – 569 + 306.
U-блоки перемычек по длине: 400 – 31,3 м, 240 – 14,4 м.

						Г210-АР	
						Индивидуальный жилой дом Г-210 (демонстрационный эскиз)	
Изм.	Кол.уч	Лист	№ док.	Подп.	Дата		
Разраб.						Жилой дом из газобетона, 206,5 м2	Стадия: П; Лист: 4; Листов: 4
Пров.							
Н. контр.						Развёртки стен по осям А и 1	Организация
ГИП							

Взам. инв. №

Подп. и дата

Инв. № подл.

Формат А2